



CITY OF MANCHESTER
PLANNING AND COMMUNITY DEVELOPMENT

Planning and Zoning
Building Regulation
Code Enforcement
Community Improvement Program

Jeffrey D. Belanger, AICP
Director

Nicola Strong
Deputy Director, Planning & Zoning

Michael J. Landry, PE, Esq.
Deputy Director, Building Regulations

August 31, 2026

Dennis and Debra Villiard (Owner)
50 Delia Drive
Manchester, NH 03102

RE: ZBA2026-072, 50 Delia Drive, B-2


Zoning Relief Required for Building Permit

Your application for a permit dated **July 27, 2026** to construct a **16' x 26' two-story addition to an existing detached two-story garage with an ADU on the second floor which will add approximately 416 SF and two bedrooms to the ADU which will result in a three-bedroom, single-family dwelling of 1,230 SF and a planned development with two principal structures on the lot, where the primary façade entrance is located on the second floor, where first-story primary façade transparency is 3.5% where 10% is required and with a blank wall of 18' where 15' is allowed in the R-1B Zoning District,** all as per documents submitted through **July 30, 2026** and with non-compliance listed in the Zoning Review dated **July 27, 2026** is hereby acknowledged.

According to Section(s) **5.3.1.A.2.A Entrance Types Required, 5.3.1.A.6.A Minimum Transparency of First-Story Primary Façade, and 5.3.1.A.6.B Blank Wall Limitations for Primary Façade** of the Zoning Ordinance of the City of Manchester, New Hampshire, passed to be ordained on March 1, 2026, this is prohibited. Consequently, I have no authority to grant this permit. Permit is hereby DENIED.

Required Actions: Planned Development Approval

Further proceedings contemplated pertaining to this application must be pursuant to NH Revised Statutes Annotated 674:33 or the other statutory provisions relative to Zoning Boards of Adjustment, as may be appropriate.

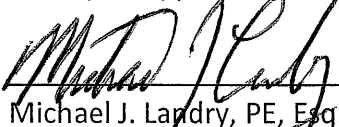

Michael J. Landry, PE, Esq.
Deputy Director, Building Regulations

B....#330....'78....Albert Lemay

Htg.....#586.....10/3/88.....Robert Bartlett

Research done 10/5/90, show a single family w/garage,
Per old bldg permit, assessors, city directory.

H...#771...5/26/95...Home Air Plus...Robert Bartlett

(B-1)...permit denied...1/11/02....Robert Bartlett

(B-1)...appeal denied...3/7/02...C#11-ZO-02.

maintaining dwelling unit in upper story of detached

garage.

Violation notice issued 03/19/02 Re: Order to remove the
the illegal dwelling unit in the upper story of the
detached garage and obtain permit for work done to finish
area above garage.

50 DELIA DRIVE
Variance History

B-1 Case: 11-ZO-02

Maintain a dwelling unit in the upper story of a detached garage converted without benefit of a permit, resulting in two principal structures on one lot.

DENIED 03/07/2002

Robert A. Bartlett (Owner)



**CITY OF MANCHESTER, NH
ZONING BOARD OF ADJUSTMENT
ONE CITY HALL PLAZA
MANCHESTER, NH 03101-2097**

VARIANCE NOTICE OF DECISION

Case No. 11-ZO-02

Property Location: 50 Delia Dr.

You are hereby notified that the request of: Robert A. Bartlett (Owner)
50 Delia Dr.
Manchester, NH 03102-8519

For a **variance** from the terms of Section 5.08 (multiple structures) of the Manchester, NH Zoning Ordinance.
Zoning District: R-1B

Applicant proposes to maintain dwelling unit in upper story of detached garage converted without benefit of a permit and resulting in two principal structures on one lot, as per plans submitted December 21, 2001, at 50 Delia Dr.

has been Denied in accordance with Article V of the Board's BY-LAWS.

Stipulations or Comments: _____

Based on the information before the Board, the applicant has not met his/her burden of proof in showing:

1. The requested use does not cause diminution in value of surrounding properties to be suffered. _____
- * 2. Granting the permit would not be contrary to the public interest. The apartment above the garage does not fall under the "in-law apartment" criteria as described in the Zoning Ordinance.
3. Denial of the permit would result in unnecessary hardship to the owner seeking it. _____
- * 4. By granting the permit substantial justice would be done. Owner is in violation of approved permit which allowed the second story of the garage to be used for storage.
- * 5. The use must not be contrary to the Spirit of the Ordinance. It would be contrary to the Spirit of the Zoning Ordinance to allow two dwelling units in the R-1B zone.

[Signature]
Chairman, Zoning Board of Adjustment

March 7, 2002

Date

ZONING REVIEW

Reviewed By: Jim Tierney
Revised By: Glenn Gagne

Date: 7/29/2026
Date Revised: 13-Jul-26

Applicant Name: Dennis Villiard
Street Address: 50 Delia Drive
Secondary Frontages (if any): Front Street

Submission Date: 7/27/2026
Street Status: Presumed R.O.W
Map / Lot: 768 - 31
Alley Access: NO
Ward: 12

Base Zone: R-1B (Residential One Family - High Density)

Building Type: House

Overlay District: Manchester Landfill Groundwater Management Zone Overlay (ML-GMZ)

Planning Department / Board Action

- ☐ Site Plan
☐ Subdivision
☒ Planned Development
☐ Conditional Use Permit
☐ Voluntary Merger

Additional Overlays

- ☐ Airport Approach
☐ Airport Noise
☐ Airport Navigational Hazard
☐ FEMA Flood Plain

Additional Review Required

- ☐ Conservation Commission
☐ Regional Impact
☐ Heritage Commission

Dimensions	Existing	Proposed
Area of Lot (Square Feet)	29,013	29,013
Area of Building on Lot (Square Feet)	820 & 720	820 & 1104
Number of Stories	1.75 & 2	1.75 & 2
Total Area of All Floors (Square Feet)	1,306 & 814	1,306 & 1,228

Article 4 Uses	Permitted Per	Not Permitted Per	Remarks
☐ Single Family Dwelling(s)	Table 4.3.1-A		Two-(2) Single Family Dwellings on the same lot.
☐			
☐			
☐			

Article 4 Additional Requirements Per Use	Section	Permitted/ Required	Proposed/ Existing	Remarks
☐				
☐				
☐				
☐				
☐				
☐				
☐				
☐				

Article 5		Section	Permitted/ Required	Proposed/ Existing	Remarks
Dimensional Requirements					
☐	Minimum Lot	Front-Loaded	8.7.2 (C)	100'	149.89 ft. *See PD Review Sheet
☐	Width	Alley-Loaded	8.7.2(C)	100'	
☐	Maximum Lot Width at Frontage		5.3.1.A.3.A	N/A	*See PD Review Sheet
☐	Lot Depth		5.3.1.A.3.B	100 ft.	*See PD Review Sheet
☐	Front/Street	Minimum	5.3.1.A.3.C	20 ft.	52 ft. *See PD Review Sheet
☐	Yard Setback	Maximum	5.3.1.A.3.C	N/A	
☐	Minimum Side Yard Setback		8.7.2 (B) 2	20 ft.	*See PD Review Sheet
☐	Minimum Side Yard Setback		8.7.2 (B) 2	20 ft.	*See PD Review Sheet
☐	Minimum Rear Yard Setback		5.3.1.A.3.F	20 ft.	*See PD Review Sheet
☐	Minimum Buildable Lot Area		5.3.1.A.3.G	12,000 SF	*See PD Review Sheet
☐	Maximum Lot Coverage		5.3.1.A.3.H	60%	*See PD Review Sheet
☐	Uses Within Floors	First Floor	5.3.1.A.4.A	Residential	Residential OK
☐		Upper Floors	5.3.1.A.4.A	Residential	Residential OK
☐	Maximum Number of Dwelling Units per Building		5.3.1.A.4.C	1 + 1 ADU	1 DU & 1DU OK
☐	Additional Lot Area Required for Residential Uses		-	N/A	
☐	House Building Type / Max. of 2		5.3.1.A.7.C.	2	2 OK
☐	Specific Standards		5.3.1.A.7		
☐	Other				

Article 5		Section	Permitted/ Required	Proposed/ Existing	Remarks
Height Requirements					
☐	Minimum Height in Stories		5.3.1.A.5.A	1 Story	2 & 1.5 OK
☐	Maximum Height in Stories		5.3.1.A.5.B	2.5 Stories	
☐	Maximum Height in Feet		5.3.1.A.5.C	35 ft.	Less OK
☐	Minimum First Story Height		-	N/A	

Article 5 Street Façade Requirements			Section	Permitted/ Required	Proposed/ Existing	Remarks
☒	Entrance Types - One Required		5.3.1(A)2(A)	Porch, Recessed Porch, Step, Recessed Entry	See Plan	N/C - See Section 5.4.2
☐	Street Façade Elements		5.4.2.B	N/A		
☒	Minimum Transparency per Façade	First Story - Primary	5.3.1.A.6.A	10%	3.50%	N/C
☐		First Story - Secondary	5.3.1.A.6.A	10%	Existing	OK
☐		Upper Stories	5.3.1.A.6.A	10%	10.11%	OK - 2 windows & 1-9 lite door
☒	Blank Wall Limitations	Primary Façade	5.3.1.A.6.B	15 ft. max.	18 ft.	N/C
☐		Secondary Façade	5.3.1.A.6.B	15 ft. max.	Existing	OK
☐	Number of Street Entrances		5.3.1.A.6.D	Min. 1 entrance per unit	1	OK
☐	Roof Types		5.4.6.E	Pitched	Pitched	OK
☐	Façade Variety		5.4.6.F	Not Required		
☐	Building Materials		-	N/A		

Article 5 Accessory Structures			Section	Permitted/ Required	Proposed/ Existing	Remarks
☐	Setback	Front/Street Yards	5.6	20 ft.	None	OK
☐		Side Yard		Match Primary Structure	Existing	OK - **No permits on file
☐		Rear Yard		4 ft.	N/A	
☐	Height	Side Yard	5.6	15 ft.	Less	OK
		Rear Yard			N/A	
☐	Size Limits	Side Yard	5.6			
		Rear Yard				
☐	Special Requirements		5.6			

Article 7 Parking Requirements		Section	Permitted/ Required	Proposed/ Existing	Remarks
☐	Surface Parking Location	5.3.1.A.3.I	All Yards	See Plan	*See PD Review Sheet
☐	Garage Location	5.3.1.A.3.J	Rear, Side or Secondary Street Yard	See Plan	*See PD Review Sheet
☐	Parking, Number of Spaces	Table 7.2-A	2	2	OK - Garage
☐	Parking Surfaces	7.3.2	Required	Proposed	OK
☐	Maximum Driveway Width	7.4.2.A	24'	14 ft.	OK
☐	Parking, Setbacks, From Lot Lines	7.5.1.A	See Ord.	See Plan	OK
☐	Parking, Setbacks, From Building	7.5.1.A	See Ord.	See Plan	OK
☐	Parking, Principal Frontage	7.5.1.B.2	See Ord.	See Plan	OK
☐	Parking, Tandem	7.5.1.C		N/A	
☐	Parking, Safety of Design	-	See Ord.	See Plan	OK
☐	Parking Lot Perimeter Landscape	8.1.3	N/A		
☐	Parking Lot Interior Landscape, Percent	8.1.5.A	N/A		
☐	Parking Lot Interior Landscape, Tree Distribution	8.1.5.B	N/A		
☐	Landscape Islands	Distribution	8.1.5.C.1	N/A	
☐		Island Dimensions	8.1.5.C.2	N/A	
☐		Shade Trees Required	8.1.5.C.3	N/A	
☐	Landscape Islands	Distribution	8.1.5.C.1	N/A	
☐		Island Dimensions	8.1.5.C.2	N/A	
☐		Shade Trees Required	8.1.5.C.3	N/A	
☐	Parking Lot Interior Landscape, Stormwater Integration	8.1.5.E	N/A		
☐	Parking, Bumpers	-	N/A		
☐	Parking, Demarcation	7.5.1.C.2		N/A	
☐	Parking, Illumination	-	N/A		
☐	Stacking, Number of Spaces	Table 7.5.3-A		N/A	
☐	Stacking, Design	7.5.3.C			
☐	Loading, Number of Spaces	Table 7.5.4-A		N/A	
☐	Loading, Location	7.5.4.B			
☐	Loading, Screening	7.5.4.D			
☐	Loading, Dimensions	7.5.4.E			
☐	Number of Accessible Parking Spaces	Table 7.6-A		N/A	
☐	Accessible Parking Space, Dimensions	7.6.5 & 7.6.6			

Parking Space Requirements Building Use	Unit of Measurement	Computation	Spaces Required
Single Family Dwelling	1 per Unit	2 Units x 1 = 2	2
		TOTAL:	2

Article 6 Special District-Wide Regulations		Section	Permitted/ Required	Proposed/ Existing	Remarks
☐	Limited Activity Buffer	6.4.2			
☐	Wetlands, No-Touch Buffer	6.4.3.C	10 ft.	N/A	
☐	Standard Structural Setback		25 ft.		
☐	Wetlands, No-Touch Buffer	6.4.3.D	25 ft.	N/A	
☐	High Priority Structural Setback		50 ft.		
☐	*Other*	6.4			

Article 8 Site and Landscaping Standards		Section	Permitted/ Required	Proposed/ Existing	Remarks
☐	Landscaping, Minimum Planting Size	8.1.1.D		N/A	
☐	Landscaped Buffer Yards, Buffer Yard Type Standards	Table 8.1.2-A		N/A	
☐	Landscaped Buffer Yards, District Boundaries	Table 8.1.2-B		N/A	
☐	Landscaped Buffer Yards, Use Abutting R or MX District Boundaries	Table 8.1.2-C		N/A	
☐	Fences and Walls	8.2			
☐	Fence Height	Table 8.2.4-A	4 ft.	Existing	OK - Chainlink in street yard
☐			6 ft.	Existing	OK - 4' chainlink
☐			8 ft.	N/A	
☐	Height of Fences on Walls	8.2.4.A	4 ft.	None	OK - No fence on wall
☐	Setback of Retaining Walls > 4 ft.	8.2.4.B	10 ft.	Existing	OK - Under 4' tall
☐	Screening of Dumpster & Utilities	Table 8.3-A		N/A	
☐	Visibility at Intersections	8.4	30 ft.	N/A	
☐	Site Lighting Standards	8.5	See Ord.	See Plan	OK -
☐	Open Spaces	8.6			

Section 8.7: Planned Developments	Proposed/ Existing	Remarks
☒	Proposed	OK

*See Planned Development Standards Review Sheet

Article 9: Sign Standards	Proposed/ Existing	Remarks
☐	None	OK

*See Sign Standards Review Sheet

Additional Information: ** Note: When reviewing the property permit history, I could not locate permits on file for the replacement of round to oval pool, pool deck, shed north of the primary dwelling or gazebo shown on the plan and a 2024 permit (RESALT2024-0735) to repair fire damaged garage / ADU has not receive a Certificate of Occupancy.	

PLANNED DEVELOPMENT REVIEW

Reviewed By: Jim Tierney
Revised By: Glenn Gagne

Date: July 30, 2026
Revision Date: July 13, 2026

Applicant Name: Dennis Villiad
Street Address: 50 Delia Drive
Secondary Frontages (if any): Front Street

Submission Date: 7/27/2026
Street Status: Presumed R.O.W
Map / Lot: 768 - 31
Alley Access: NO
Ward: 12

Base Zone: R-1B (Residential One Family - High Density)

Type: Residential PD

Building Type

Closest to Street: Other

Parcel Area: <5 acres

Article 8 Planned Development Standards		Section	Permitted/ Required	Proposed/ Existing	Remarks
☐	Building Types	8.7.1.C	House	House	Fill out regular review sheet for all building types on lot
☐	Maximum Number of Principal Buildings on Lot	8.7.1.C	2	2	PDs using House, Duplex, Triple-Decker, or Apartment House limited to 2 principal buildings
☐	Front Yard Minimum	8.7.2.B.1	20 ft.	52 ft.	OK
☐	Setback Maximum		N/A		
☐	Setback from Side and Rear Lot Lines	8.7.2.B.2	20 ft.	32 ft.	OK
☐	Separation from Other Buildings	8.7.2.B.3	20 ft.	23 ft.	OK
☐	Lot Frontage	8.7.2.C	100 ft.	149.89 ft.	OK
☐	Primary Façades of Buildings	8.7.2.D/E	See Ord.	See Plan	OK
☐	Parking Location	8.7.2.F	No front yard parking within 20 ft. front setback	See Plan	OK
☐	Parking Lot Perimeter Landscape	8.1.3		N/A	
☐	Parking Lot Interior Landscape	8.1.4 / 8.1.5		N/A	
☐	Parking, Number of Spaces	Table 7.2-A	2	2	OK
☐	Parking, Safety of Design	7.5.2.D	See Ord.	See Plan	OK
☐	Common Components	8.7.3.A		N/A	
☐	Space Contiguous Land	8.7.3.B		N/A	
☐	Standards Impervious Surfaces	8.7.3.C		N/A	
☐	Open Space Type (If Applicable)	8.6.2		N/A	

Additional Information:

Property Location 50 DELIA DR
Vision ID 24287

Account # 2109419

Map ID 0768//0031//

Bldg # 1

Bldg Name
Sec # 1 of 1

Card # 1 of 1

State Use 1010
Print Date 7/23/2026 11:39:26 A

CURRENT OWNER		TOPO		UTILITIES		STRT / ROAD		LOCATION		CURRENT ASSESSMENT								2017 MANCHESTER, NH VISION					
VILLIARD, DENNIS M 50 DELIA DR MANCHESTER NH 03102		1	Suitable	1	All Public	1	Paved	1	Urban	Description	Code	Appraised		Assessed									
		1	Level							RESIDENTL	1010	159,200		159,200									
										RES LAND	1010	101,900		101,900									
										RESIDENTL	1010	37,300		37,300									
		SUPPLEMENTAL DATA																					
		Alt Prcl ID Land Adjus NO Voided NO Total SF TIF Zone Frontage/D No GIS ID 768-31				RAD OR C CAD = 643 TIF Origina TIF Note Land Class R Parcel Zip 03102-8519 Assoc Pid#																	
										Total								298,400		298,400			
RECORD OF OWNERSHIP				BK-VOL/PAGE		SALE DATE		Q/U V/I		SALE PRICE		VC		PREVIOUS ASSESSMENTS (HISTORY)									
VILLIARD, DENNIS M BARTLETT, ROBERT A BARTLETT, ROBERT A BARTLETT ARTHUR J WASHINGTON PARK ESTATES REALTY				7063	1704	09-10-2003	U	I	225,000	00		Year	Code	Assessed	Year	Code	Assessed V	Year	Code	Assessed			
				5440	0368	05-29-1993	U		4,000	04	2025	1010	159,200	2024	1010	159,200	2023	1010	159,200				
				0	0	11-01-1985			0			1010	101,900		1010	101,900		1010	101,900				
				0	0	09-06-1985			0			1010	37,300		1010	37,300		1010	37,300				
				0	0	06-15-1984			0														
												Total		298,400		Total		298,400		Total		298,400	
EXEMPTIONS				OTHER ASSESSMENTS								This signature acknowledges a visit by a Data Collector or Assessor											
Year	Code	Description		Amount		Code	Description		Number	Amount		Comm Int											
Total				0.00																			
ASSESSING NEIGHBORHOOD																							
Nbhd		Nbhd Name		B		Tracing		Batch															
550																							
NOTES																							
C/A 1ST FLOOR ONLY FGR4=2ND FL FULL FIN WITH FULL BATH AND RECREATION AREA + CENTRAL AIR FGR AREA=24 X 30										APT AREA=28 X 30 LISTED @ 26 X 30													
BUILDING PERMIT RECORD										VISIT / CHANGE HISTORY													
Permit Id	Issue Date	Type	Description	Amount	Insp Date	% Comp	Date Comp	Comments		Date	Id	Type	Is	Cd	Purpost/Result								
04-03576	07-01-2004	RS	Residential	4,038				ABOVE GROUND POOL		06-14-2011	RK			99	Field Review Change								
04-01503	04-05-2004	RS	Residential	650				BUILD SHED		03-31-2006	SC			00	Meas & Int Insp.								
										12-14-2005	DI			01	Meas/Int Estimate								
										12-14-2005	DI			02	2nd Visit Not Home								
										08-11-2000	JR			07	Meas/Info@Dr								
										09-21-1990				20	Sale Inspection								
LAND LINE VALUATION SECTION																							
B	Use Code	Description	Zone	Land Type	Land Units	Unit Price	I. Factor	Site Index	Cond.	Nbhd.	Nbhd. Adj	Notes		Location Adjustment		Adj Unit P	Land Value						
1	1010	SINGLE FAM			57,935 SF	2.07	1.00000	1	1.00	550	0.850				1.0000	1.76	101,900						
Total Card Land Units					1	AC	Parcel Total Land Area					1	Total Land Value					101,900					

Property Location 50 DELIA DR
Vision ID 24287

Account # 2109419

Map ID 0768//0031//

Bldg # 1

Bldg Name
Sec # 1 of 1

Card # 1 of 1


State Use 1010
Print Date 7/23/2026 11:39:27 A


CONSTRUCTION DETAIL			CONSTRUCTION DETAIL (CONTINUED)		
Element	Cd	Description	Element	Cd	Description
Style:	04	Cape Cod			
Model	01	Residential			
Grade:	03	Average			
Stories:	1.75	1 3/4 Stories			
Occupancy	1				
Exterior Wall 1	25	Vinyl Siding			
Exterior Wall 2					
Roof Structure:	03	Gable/Hip			
Roof Cover	03	Asphalt			
Interior Wall 1	03	Plastered			
Interior Wall 2	05	Drywall			
Interior Flr 1	14	Carpet			
Interior Flr 2					
Heat Fuel	02	Oil			
Heat Type:	05	Hot Water			
AC Type:	03	Central Air			
Total Bedrooms	02	2 Bedrooms			
Total Bthrms:	2				
Total Half Baths	0				
Total Xtra Fixtrs					
Total Rooms:	5	5 Rooms			
Bath Style:	02	Average			
Kitchen Style:	02	Average			
MHP					

CONDO DATA			
Parcel Id		C	Owne
		B	S
Adjust Type	Code	Description	Factor%
Condo Flr			
Condo Unit			
COST / MARKET VALUATION			
Building Value New		244,897	
Year Built		1938	
Effective Year Built		1986	
Depreciation Code		GD	
Remodel Rating			
Year Remodeled			
Depreciation %		35	
Functional Obsol		0	
External Obsol		0	
Trend Factor		1	
Condition			
Condition %			
Percent Good		65	
RCNLD		159,200	
Dep % Ovr			
Dep Ovr Comment			
Misc Imp Ovr			
Misc Imp Ovr Comment			
Cost to Cure Ovr			
Cost to Cure Ovr Comment			

OB - OUTBUILDING & YARD ITEMS(L) / XF - BUILDING EXTRA FEATURES(B)										
Code	Description	L/B	Units	Unit Price	Yr Blt	Cond. Cd	% Gd	Grade	Grade Adj.	Appr. Value
FGR7	GARAGE W/ A	L	780	62.00	2016		75		0.00	36,300
SPL4	ABOVE GR R	L	24	300.00	2016		0		0.00	0
SHD2	W/LIGHTS ET	L	120	16.00	2016		50		0.00	1,000

BUILDING SUB-AREA SUMMARY SECTION						
Code	Description	Living Area	Floor Area	Eff Area	Unit Cost	Undeprec Value
BAS	First Floor	820	820	820	170.30	139,649
TQS	Three Quarter Story	486	648	486	127.73	82,768
UBM	Basement, Unfinished	0	660	132	34.06	22,480
Ttl Gross Liv / Lease Area		1,306	2,128	1,438		244,897

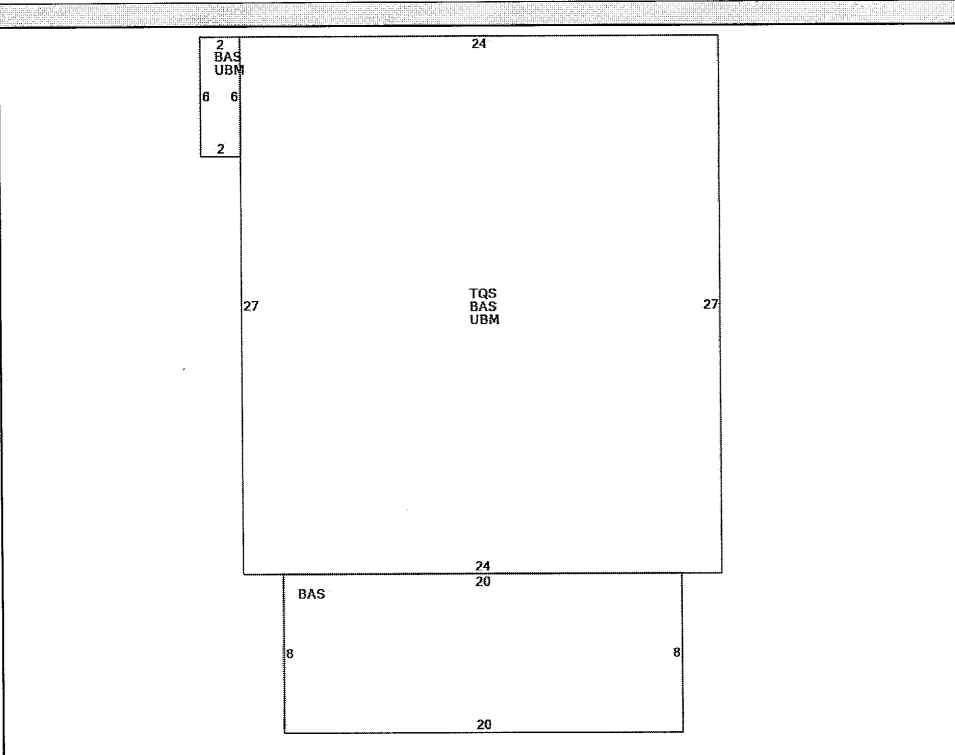

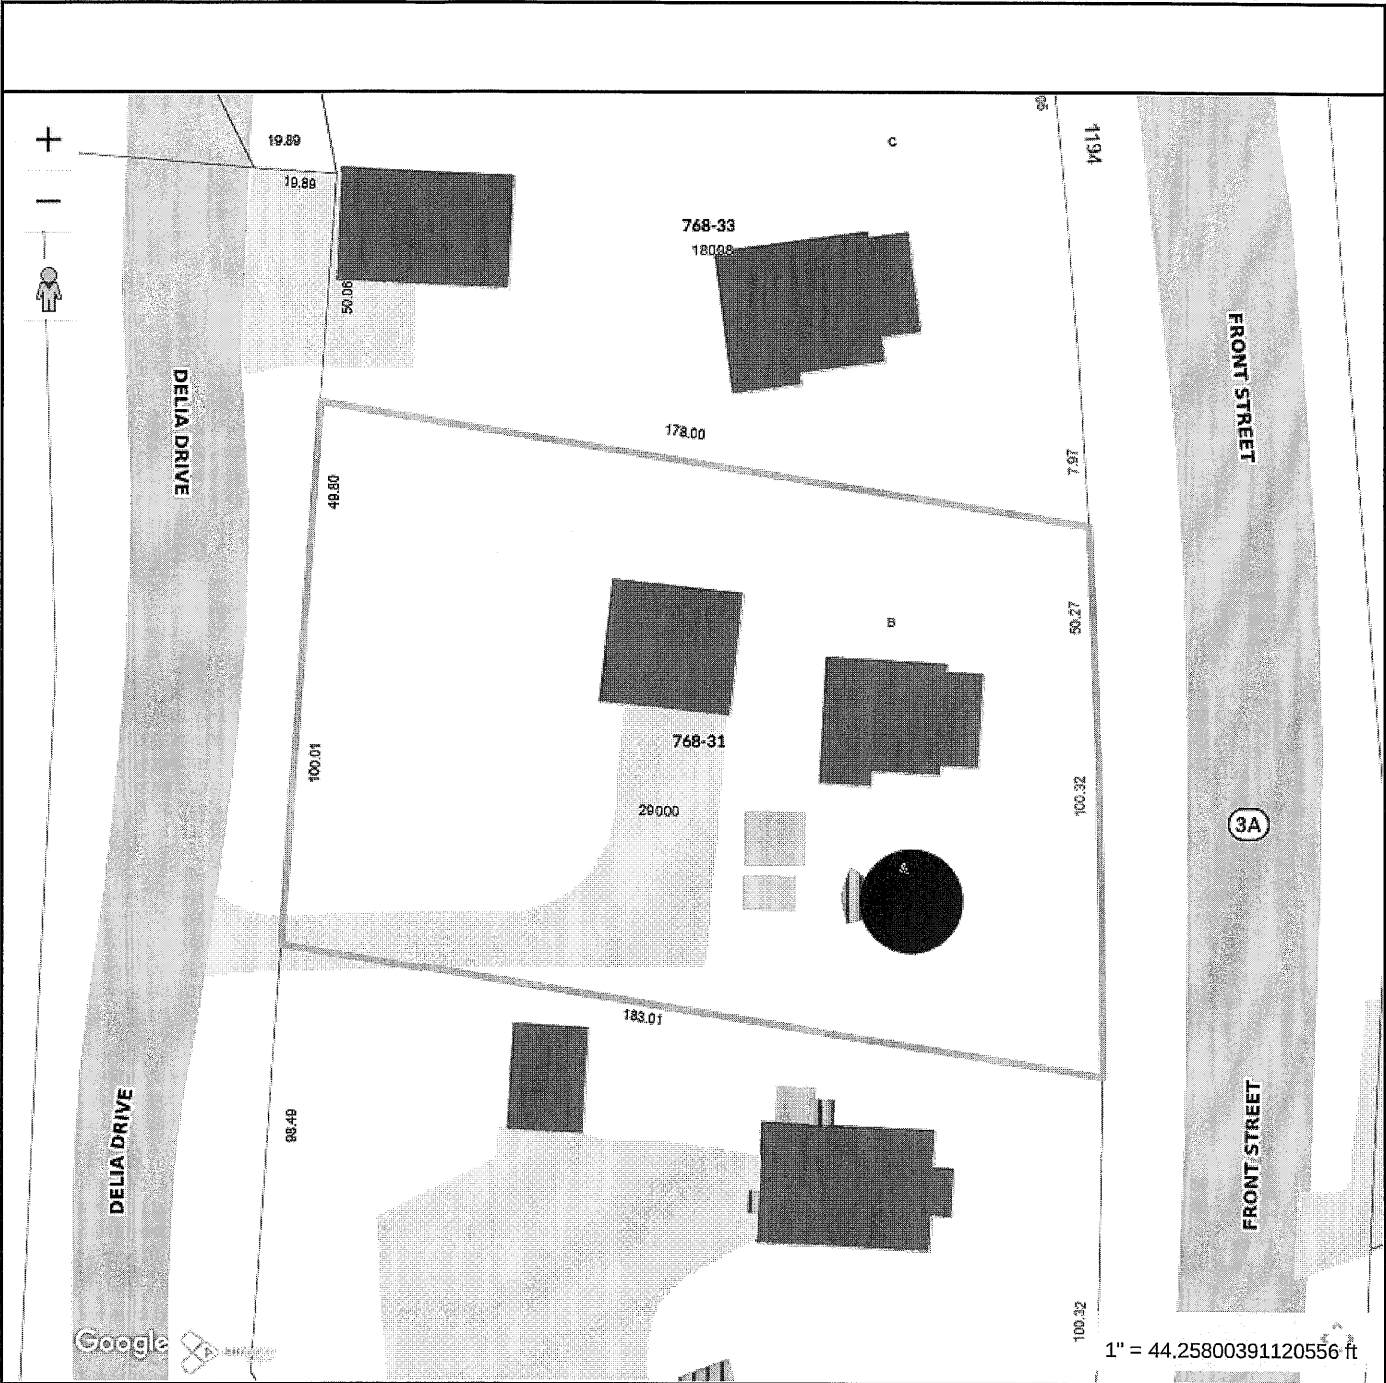

Property Information	
ParcelID	0768-0031
Location	50 DELIA DR
Owner	VILLIARD, DENNIS M



**MAP FOR REFERENCE ONLY
NOT A LEGAL DOCUMENT**

City of Manchester, NH makes no claims and no warranties, expressed or implied, concerning the validity or accuracy of the GIS data presented on this map.

Geometry updated Daily
Data updated Daily

Print map scale is approximate.
Critical layout or measurement activities should not be done using this resource.



City of Manchester
Planning & Community Development
One City Hall Plaza-West Wing
Manchester, NH 03101
(603) 624-6475
www.manchesternh.gov

Jeffrey D. Belanger, AICP
Director

Pamela H. Goucher, AICP
Deputy Director Planning & Zoning

Michael J. Landry, PE, Esq.
Deputy Director Building Regulations

VARIANCE CRITERIA

Complete this form and attach 10 copies along with any supplemental material that would support your appeal.

Deadline for Next Hearing: _____

Property Location: 50 Delia Drive Manchester, NH 03102

Owner: Dennis and Debra Villiard

Address: 50 Delia Drive
Manchester, NH 03102

Phone #: _____

Email: _____

Applicant: Dennis + Debra Villiard

Address: 50 Delia Dr.
Manchester, NH 03102

Phone #: _____

Email: _____

Relief Sought From Section(s): _____

1. The variance would not be contrary to the public interest because: _____

2. The spirit of the ordinance is observed because: SEE ATTACHED

3. Substantial justice would be done because: _____

4. The values of surrounding properties would not be diminished because: _____

5. Literal enforcement of the provisions of the ordinance would result in unnecessary hardship if:

(A) Owing to the following special conditions of the property that distinguish it from other properties in the area:

- No fair and substantial relationship exists between the general purposes of the ordinance provisions and the specific application of that provision to the property; and
- The proposed use is a reasonable one.

Or (B) Owing to the following special conditions of the property that distinguish it from other properties in the area, the property cannot be reasonably used in strict conformance with the ordinance, and a variance is therefore necessary to enable a reasonable use of it.

Dennis M Villiard
Applicant Signature

Dennis M. Villiard
Print Name

7/27/2026
Date

Variance Criteria Villiard 50 Delia Drive July, 2026

Sections of the Zoning Ordinance Needing Relief:

The existing garage/ADU is existing non-conforming with respect to being in a street yard.

1. The variance would not be contrary to the public interest because:

Granting variance would not be contrary to the public interest because it will not alter the essential character of the neighborhood. The purpose of the addition of two rooms to the existing garage/ADU structure is to provide diverse affordable housing without the need for additional infrastructure or land development. The existing garage/ADU was constructed before the applicant purchased the property. The applicant purchased the property in 2003. The addition will be the same height and width of the existing structure. This addition will not affect the distance of the current structure to the two neighbors on this dead end street. The addition will extend 16 feet from the existing structure towards the road. This would leave 57 feet of land from the structure to the road.

2. By granting the variance, the use would not be contrary to the Spirit of the Zoning Ordinance because:

The intent of the zoning ordinance is to promote the efficient development of the property, prevent overcrowding and protect the health, safety and welfare of the public. The applicant is proposing an addition of two rooms with a garage below for support. The proposed addition will not encroach further than the existing structure on either side of the property. The addition will be the same height and width of the existing structure. The requested variance would not threaten the public health, safety, or welfare, or overcrowd the neighborhood, as the lot already existed with a garage/ADU on a lot with 0.67 acres in a residential area. It is our hope that the ZBA would agree this request is reasonable and within the spirit of the ordinance and should be approved.

3. By granting the variance, substantial justice would be done because:

Approval of the variance would allow the applicant to add two rooms to an existing one bedroom ADU with one combined living space. This would allow a family to have a separate bedroom and play area for a child. We can see no benefit to the public by denying this variance request. Should the application be denied, the loss to the applicant would be substantial. Therefore, as the loss to the applicant would greatly outweigh any perceived public gain, it is our opinion that this variance should be approved.

4. The proposed use would not diminish surrounding property values because:

The value of the existing garage/ADU would increase the value and function of the property by adding two rooms to an existing two room dwelling. Approval of this variance request will not reduce the value of surrounding properties.

5. Literal enforcement of the provisions of the ordinance would result in unnecessary hardship if owing to the following special conditions of the property that distinguish it from other properties in the area because:

No fair and substantial relationship exists between the general purposes of the ordinance provisions and the specific application of that provision to the property. Also, the proposed use is a reasonable one. The proposed use is a residential addition to an existing residence in a residential area.




AS-BUILT LOCATIONS
AT 50 DELIA DRIVE
MANCHESTER, NH

PREPARED FOR:
ROBERT A. BARTLETT
50 DELIA DRIVE
MANCHESTER, NH
HCRD BK.5603 PG.0840

PLAN OF REFERENCE:

BOUNDARY PLAN - ALMON G. & RITA T. PAGE AND
ALBERT A. & JEANNE M. LEMAY, MANCHESTER, NH;
PREPARED BY THOMAS F. MORAN INC. DATED MAY
10, 1983, NOT FOUND RECORDED.


ZONING: "R-S" RESIDENTIAL SUBURBAN

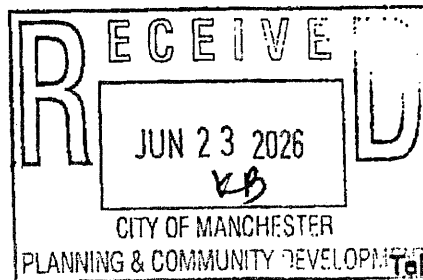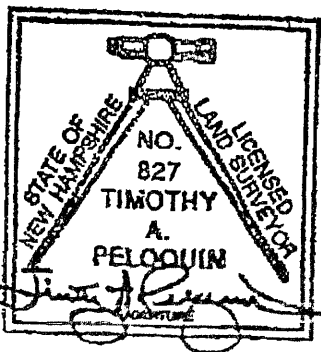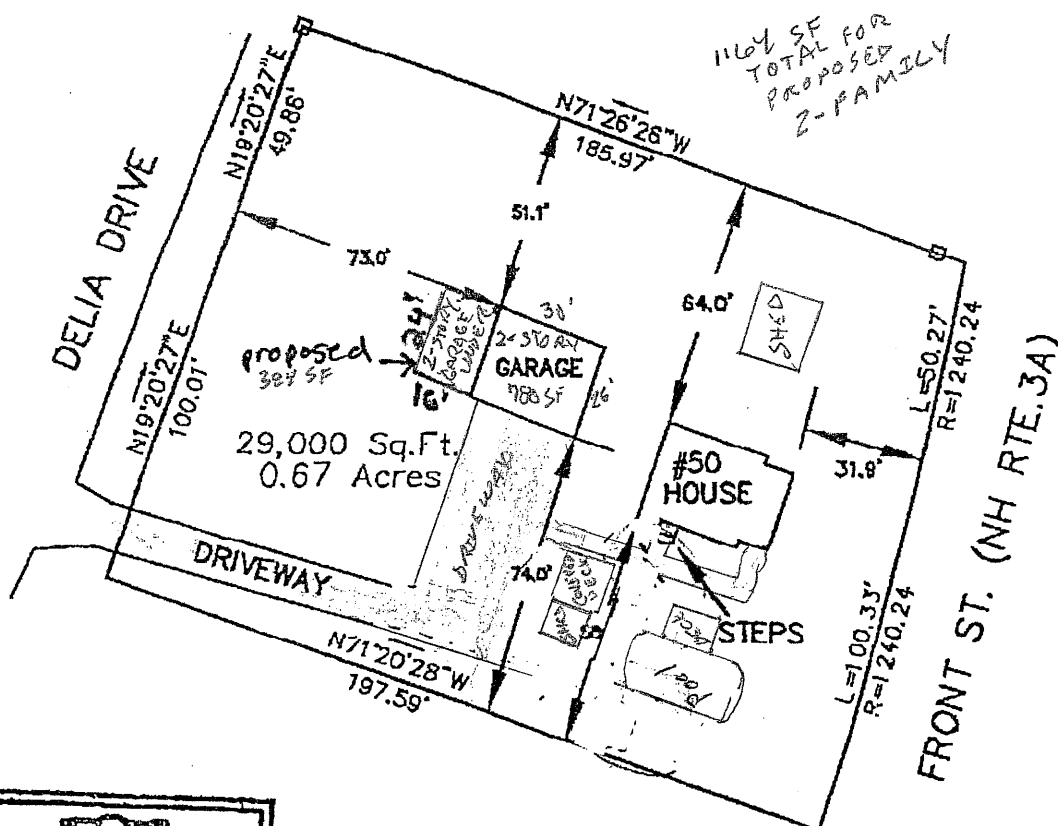


MARCH 23, 2000
SCALE: 1"=50'
Promised Land
Survey, LLC

36 Cole Road, Chester NH 03036
(603) 887-1981 Fax (603) 887-1987

ASSUMED PUBLIC R.O.W. - SEE NOTE 8

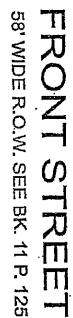

TAX MAP 768 L
PAUL GOUL
1157 FRONT ST
MANCHESTER, N
V. 7506 P.

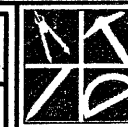

Alternative
Designs Inc.

www.alternativedesigns.net
Residential/Commercial
Design
94 Old Granite Street
Manchester, NH 03101
phone: (603) 643-4388
fax: (603) 643-6010

These drawings, specifications,
and the design concept are
the property of
Alternative Designs Inc.
Any form of reproduction of
these documents or of the
design is expressly prohibited.
A.D.I. © 2026


VILLIARD RESIDENCE
50 DELIA DR MANCHESTER, NH

ZONE 5

2021 INTERNATIONAL RESIDENTIAL CODE

ADDITION  EXISTING

PLATE HGT
MATCH EXISTING
8'-0"
SEC FLR
MATCH EXISTING
9'-11"
GARAGE
MATCH EXISTING

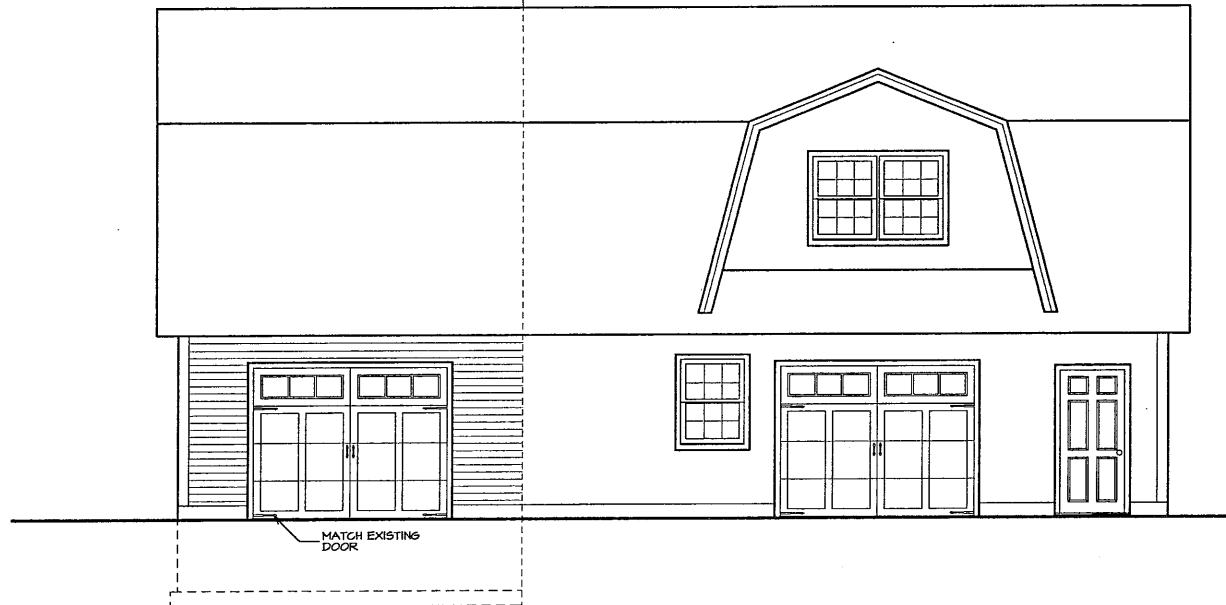

1 FRONT ELEVATION
SCALE: 1/4" = 1'-0"

NOTE:
CONTRACTOR TO VERIFY
ALL EXISTING CONDITIONS
PRIOR TO CONSTRUCTION

CODE:

- ALL CONSTRUCTION SHALL FOLLOW LOCAL STATE BUILDING CODE, MANUFACTURES' SPECIFICATIONS, AND WELL KNOWN INDUSTRY STANDARDS. IF ANY QUESTIONS SHALL ARISE, THE DESIGNER OR ENGINEER ON RECORD SHALL BE CONTACTED.
- INTERNATIONAL RESIDENTIAL CODE 2021 (IRC 2021) AND THE REFERENCED STANDARDS INCLUDED THEREIN. AHJ = AUTHORITY HAVING JURISDICTION.
 - NUMBER OF UNITS: 1 (1 OR 2)
 - NUMBER OF STORIES: 2 (MAX. 3)

DESIGN LOADS:

- UNIFORM FLOOR LIVE LOAD (NON-BEDROOM):
 - NON-BEDROOM: 40PSF
 - BEDROOM: 30PSF
 - ATTIC: 20PSF
- UNIFORM FLOOR DEAD LOAD: 15PSF
- ROOF SNOW LOAD (AHJ):
 - GROUND SNOW LOAD: 12 PSF (TOWN, STATE SPECIFIC)
 - DEAD LOAD: 10 PSF
- WIND DESIGN:
 - EXPOSURE CATEGORY: B (A-D, R301.2.1.4) (B IS NORMAL)
 - WIND SPEED ZONE (AHJ) 120 (10 - 120, MOST OF NORTHERN AND WESTERN NH AND WESTERN MA=90, CENTRAL AND SOUTH NH AND MA = 100, NH COAST, BOSTON AND SOUTH = 110, CAPE COD AND ISLANDS = 120)

5. SEISMIC

A. DESIGN CATEGORY (AHJ) (A-E, R301.2.2), (C FOR MOST OF SOUTH AND CENTRAL NH AND B FOR MA)

6. DAMAGE:

A. WEATHERING: SEVERE (CONCRETE) (R301.2.3)
B. TERMITES INFESTATION PROBABILITY: SLIGHT (NORTHERN NH), MODERATE (SOUTHERN NH), HEAVY (MA)

- DESIGN FROST DEPTH OF 4 FEET BELOW FINISHED GRADE (4' IS TYPICAL; VERIFY AS NEEDED WITH AHJ)
- WINTER DESIGN TEMP: NH: 0 DEG. F, MA 10 DEG. F. (PER 301.2(1))
- FLOOD HAZARD (AHJ): NO

GENERAL NOTES:

- THESE DRAWINGS REPRESENT AN OVERALL DESIGN CONCEPT. THEY ARE PREPARED WITH THE INTENT TO DEMONSTRATE THE OVERALL DESIGN ARRANGEMENT AND METHODS OF ASSEMBLY TO THE VARIOUS COMPONENTS. THE DRAWINGS DO NOT INDICATE EXTENSIVE DETAILS. THE CONTRACTOR SHALL HAVE REVIEWED THESE PLANS, SEEN THE SUBJECT PROPERTY, AND BE CAPABLE OF EXECUTING THE DETAIL WORK AS NECESSARY TO ACHIEVE THE INTENDED RESULT, IN A MANNER CONSISTENT WITH QUALITY WORKMANSHIP WITHIN THE REGION.
- ALL WORK SHALL BE PERFORMED IN ACCORDANCE WITH ALL APPLICABLE NATIONAL STATE AND LOCAL CODES, REGULATIONS AND FHAAVA MPS.
- CONTRACTOR SHALL VERIFY ALL CONDITIONS AND DIMENSIONS AT SITE BEFORE BEGINNING CONSTRUCTION. ANY DISCREPANCIES SHALL BE REPORTED TO ALTERNATIVE DESIGNS INC. FOR JUSTIFICATION AND OR CORRECTION BEFORE PROCEEDING WITH WORK.

- THE OWNER AND CONTRACTOR SHALL HOLD HARMLESS THE DESIGNER FROM AND AGAINST ALL CLAIMS, DAMAGES, LOSSES AND EXPENSES (INCLUDING LEGAL FEES) ARISING OUT OF OR RESULTING FROM THE PERFORMANCE OF THE WORK BY THE CONTRACTOR.
- ALL DIMENSIONS SHOULD BE READ OR CALCULATED AND NEVER SCALED.
- ALL DIMENSIONS AND CONDITIONS MUST BE VERIFIED IN THE FIELD BY THE CONTRACTOR. ANY DISCREPANCIES SHALL BE BROUGHT TO THE ATTENTION OF THE DESIGNER OR STRUCTURAL ENGINEER BEFORE PROCEEDING.
- IN THE EVENT OF A CONFLICT BETWEEN PLANS, SPECIFICATIONS, AND DETAILS, THE DESIGNER OR STRUCTURAL ENGINEER SHALL BE NOTIFIED IMMEDIATELY FOR CONSULTATION. IF CONDITIONS AT THE SITE ARE DIFFERENT THAN SHOWN, THE DESIGNER OR STRUCTURAL ENGINEER SHALL BE NOTIFIED BEFORE ANY WORK IS PROCEEDED WITH.

- ALTERNATIVE DESIGN ASSUMES NO LIABILITY AS A RESULT OF ANY CHANGES OR NON CONFORMANCE WITH THESE PLANS EXCEPT UPON THE WRITTEN APPROVAL OF THE DESIGNER OR ENGINEER ON RECORD.
- ALTERNATIVE DESIGN ASSUMES NO LIABILITY FOR WORK PERFORMED WITHOUT AN ACCEPTABLE PROGRAM OF TESTING AND INSPECTION AS APPROVED BY THE ENGINEER ON RECORD.
- REPRODUCTION OF DESIGNER PLANS AND STRUCTURAL DRAWINGS FOR SHOP DRAWINGS IS NOT PERMITTED.
- SECTIONS, DETAILS, NOTES, METHODS, OR MATERIALS SHOWN AND/OR NOTED ON ANY PLAN, SECTION OR ELEVATION SHALL APPLY TO ALL OTHER SIMILAR LOCATIONS UNLESS NOTED OTHERWISE.
- THE CONTRACTOR SHALL BE RESPONSIBLE FOR ALL SHORING AND BRACING REQUIRED DURING CONSTRUCTION. TEMPORARY SUPPORTS REQUIRED FOR STABILITY DURING ALL INTERMEDIATE STAGES OF CONSTRUCTION SHALL BE REMOVED AFTER CONSTRUCTION AND ARE THE RESPONSIBILITY OF THE CONTRACTOR.

Contractor to check & verify all dimensions & structural members before construction. All construction shall be in strict compliance with the State or National Building Codes, whichever applicable.

REVISIONS

26-195
MAY 2026
SHEET 1 OF 1

A1

DOOR SCHEDULE				
MARK	QTY	SIZE	RSO	NOTES
1		2'6" X 6'6"		9-LITE
2		6'0" X 6'6"		BIFOLD
3		2'6" X 6'6"		INTERIOR
4				
5				
6				
7				
8				
9				
10				
11				

RSO TO BE DETERMINED BY DOOR MANUFACTURER.

HEADER SCHEDULE				
SIZE	ALLOWABLE SPAN 28' BLDG WIDTH			
	NON-BRG	ROOF ONLY	1 FL. & ROOF	2 FL. & ROOF
2 - 2 X 6	6'-0"	4'-0"	NA	NA
2 - 2 X 8	8'-0"	5'-2"	4'-0"	NA
3 - 2 X 8	10'-0"	6'-5"	5'-8"	5'-4"
2 - 2 X 10	12'-0"	6'-3"	5'-6"	4'-11"
2 - 2 X 12	16'-0"	7'-3"	6'-5"	5'-4"

PROVIDE DBL JACKS FOR ALL SPANS OVER 5'-0"

WINDOW SCHEDULE				
MARK	QTY	MODEL NUMBER	RSO	NOTES
A		244DH8050		DBL HUNG
B		(2)-244DH8050		MULLION
C		244DH8040		DBL HUNG
D				
E				
F				
G				
H				
J				
K				

NOTES:

1. RSO TO BE DETERMINED BY WINDOW MANUFACTURER.
2. BEDROOM WINDOWS TO MEET EGRESS
3. IN ACCORDANCE WITH I.R.C.(2021)-R312.2, WHERE THE OPENING OF AN OPERABLE WINDOW IS MORE THAN 12" ABOVE THE EXT. FINISHED GRADE OR EXT. DECK BELOW, THE LOWEST PART OF THE CLEAR OPENING IS TO BE A MIN. OF 24" ABOVE THE FIN. FLR.
4. WINDOWS ARE BASED ON ANDERSEN 200 SERIES TILT-WASH MODEL NUMBERS

EGRESS WINDOWS

SECTIONS R-310 EMERGENCY ESCAPE AND RESCUE REQUIRED

BASEMENTS, HABITABLE ATTICS AND EVERY SLEEPING ROOM SHALL HAVE AT LEAST ONE OPERABLE EMERGENCY ESCAPE AND RESCUE OPENING. WHERE BASEMENTS CONTAIN ONE OR MORE SLEEPING ROOMS, EMERGENCY EGRESS AND RESCUE OPENINGS SHALL BE REQUIRED IN EACH SLEEPING ROOM. WHERE EMERGENCY AND RESCUE OPENINGS ARE PROVIDED, THEY SHALL HAVE A SILL HEIGHT OF NOT MORE THAN 44" ABOVE THE FLOOR.


MINIMUM OPENING AREA

ALL EMERGENCY ESCAPE AND RESCUE OPENINGS SHALL HAVE A MINIMUM NET CLEAR OPENING OF 5.7 SQUARE FEET (0.530 M2).

MINIMUM OPENING HEIGHT, THE MINIMUM NET CLEAR OPENING HEIGHT SHALL BE 24 INCHES (610 MM).

MINIMUM OPENING WIDTH, THE MINIMUM NET CLEAR OPENING WIDTH SHALL BE 20 INCHES (508 MM).

OPERATIONAL CONSTRAINTS, EMERGENCY ESCAPE AND RESCUE OPENINGS SHALL BE OPERATIONAL FROM THE INSIDE OF THE ROOM WITHOUT THE USE OF KEYS OR TOOLS.

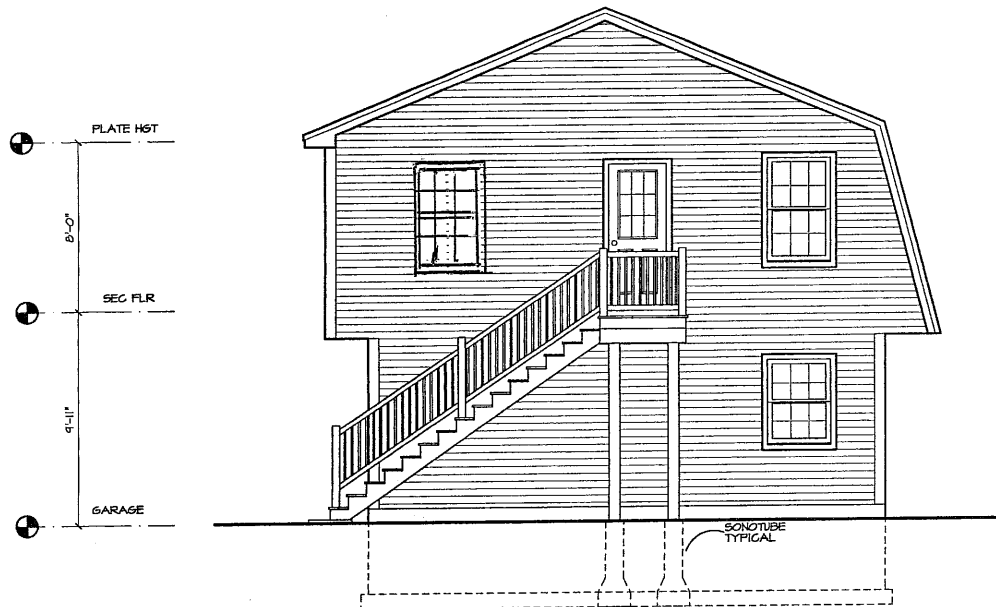

1 LEFT SIDE ELEVATION
A3 SCALE: 1/4" = 1'-0"



Alternative
Designs Inc.

www.alternativedesigns.net
residential/commercial


Design
94 Old Granite Street
Manchester, NH 03101
phone: (603) 645-4388
fax: (603) 645-6010

These drawings, specifications, and the design contained are the property of Alternative Designs Inc. Any form of reproduction of these documents, or of the design is expressly prohibited. A.D.I. © 2026

Contractor to check & verify all dimensions & structural members before construction. All construction shall be in strict compliance with The State of New Hampshire or Massachusetts Building Codes, whichever applicable.


26-195
MAY 2026
SHEET 3 OF 4

A3

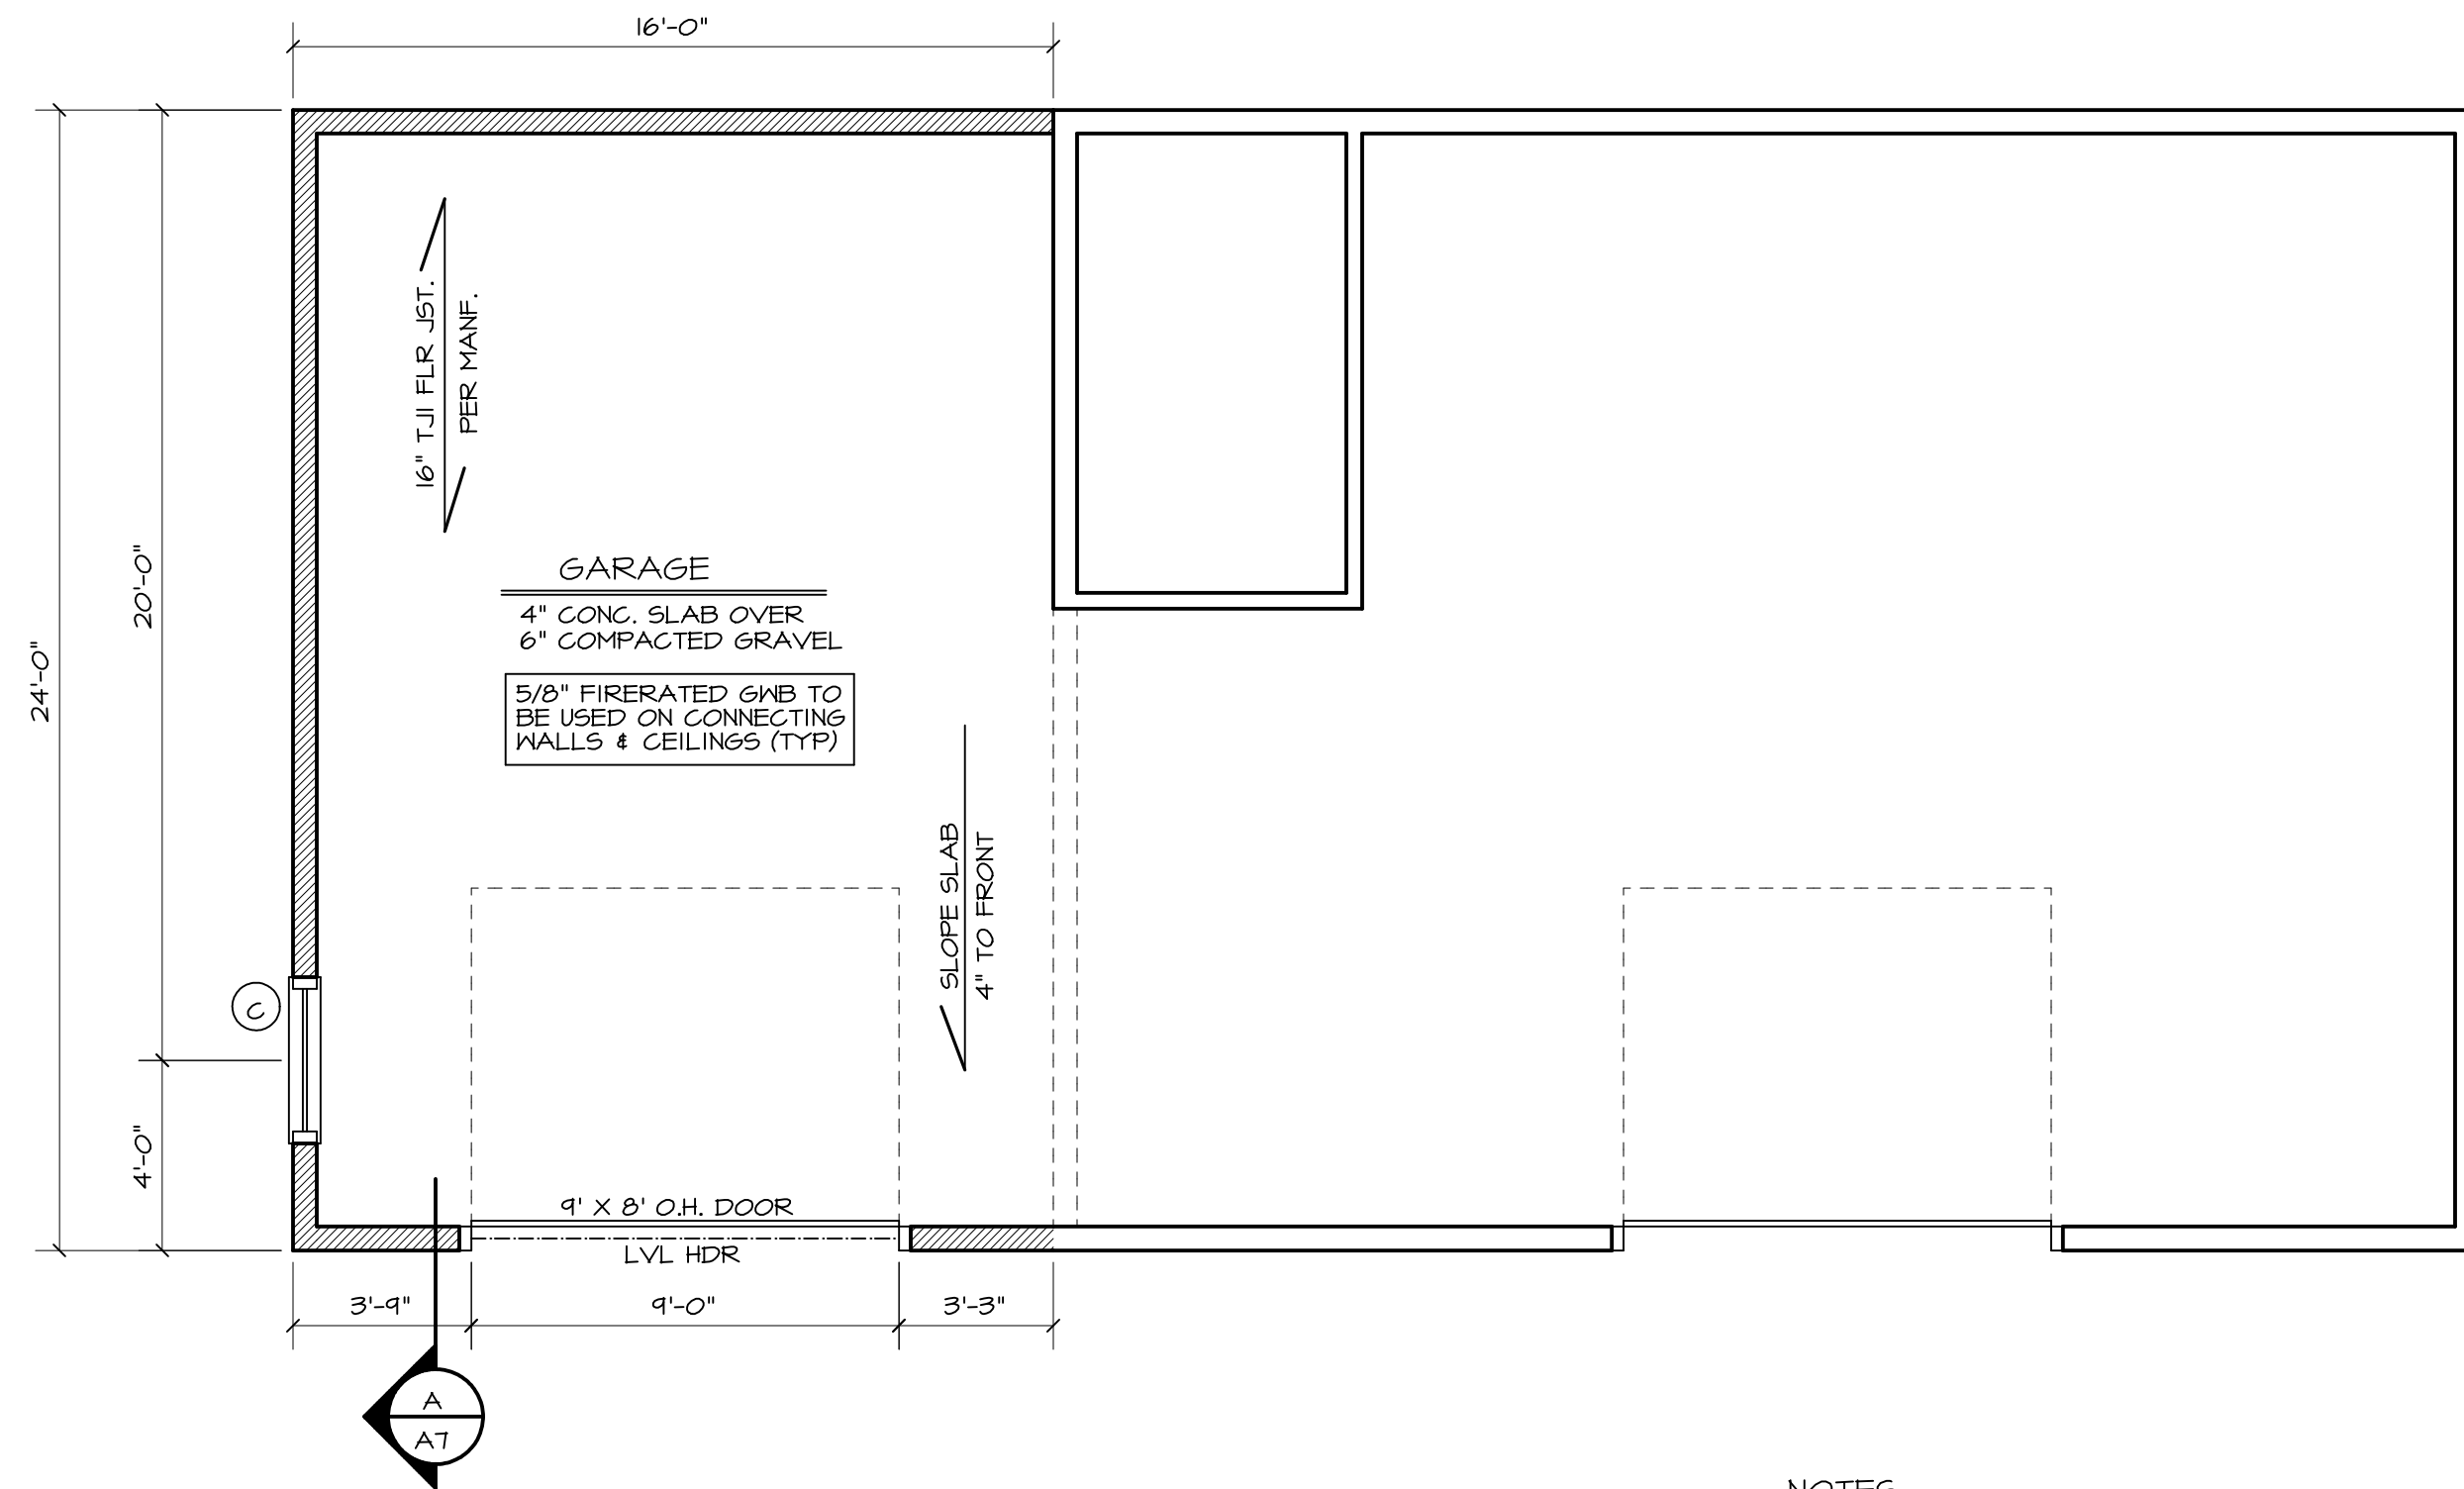

NOTES

 DENOTES NEW WALLS

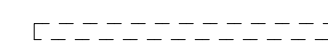 DENOTES WALLS TO BE REMOVED


NOTE:

1. PROVIDE HANDRAIL AT EACH STAIRWAY WITH 4 OR MORE RISERS R311.7.8

WIND BRACING NOTE: PROVIDE DIAGONAL WIND BRACING AT ALL OUTSIDE CORNERS. AT CORNERS WITH LESS THAN 48" OF PANEL WALL, USE ALTERNATE BRACING PANELS IN ACCORDANCE WITH INTERNATIONAL BUILDING CODE FIGURE R602.10.2.2

1 FIRST FLOOR PLAN
A4 SCALE: 1/4" = 1'-0"

NOTE:
CONTRACTOR TO VERIFY
ALL EXISTING CONDITIONS
PRIOR TO CONSTRUCTION

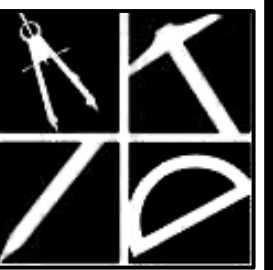

Alternative
Designs Inc.

www.alternativedesigns.net

Residential/Commercial
Design

94 Old Granite Street
Manchester, NH 03101

phone: (603) 645-4388

fax: (603) 645-6010

These drawings, specifications,
and the design conveyed are
the exclusive property of
Alternative Designs Inc.
Any form of reproduction of
these documents, or of this
design is expressly prohibited.
A.D.I. © 2026


Contractor to check & verify all
dimensions & structural members
before construction.
All construction shall be in strict
compliance with The State of
New Hampshire or Massachusetts
Building Codes, whichever applicable.

REVISIONS

26-195

MAY 2026


SHEET 4 OF 4

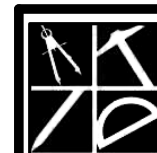

Alternative
Designs Inc.

26-195

A4

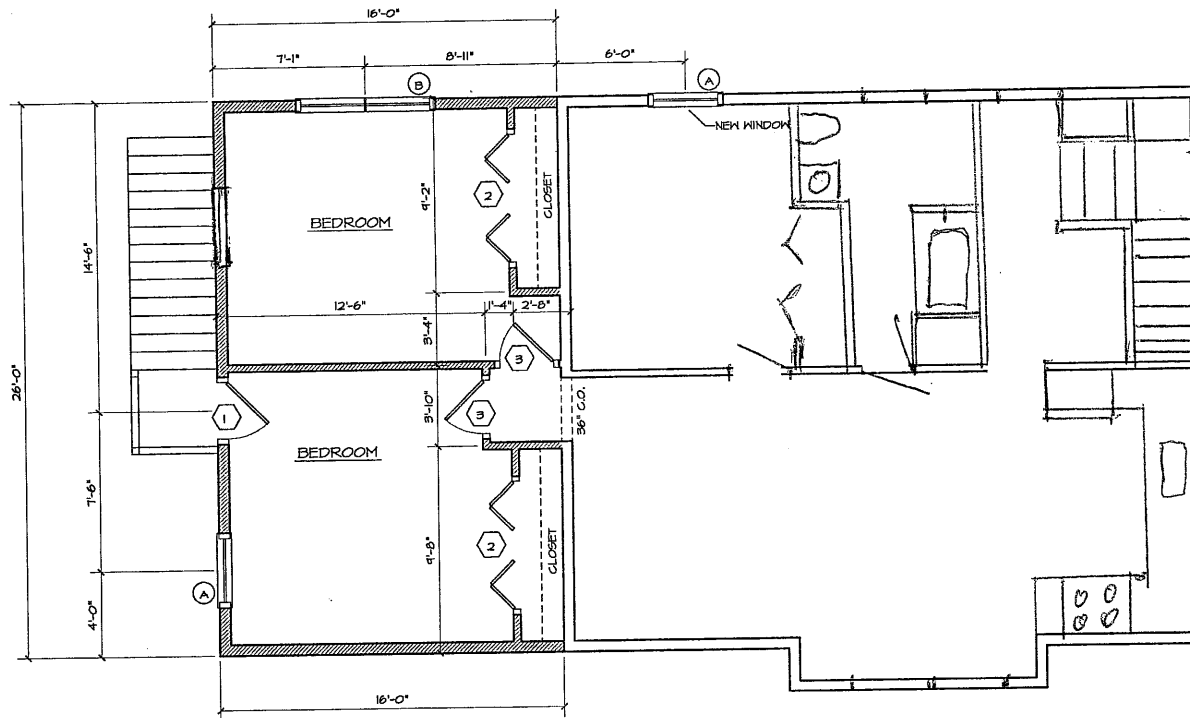

NOTES

--- DENOTES NEW WALLS


--- DENOTES WALLS TO BE REMOVED

1 SECOND FLOOR PLAN
A5 SCALE: 1/4" = 1'-0"

NOTE:

1. PROVIDE HANDRAIL AT EACH STAIRWAY WITH 4 OR MORE RISERS R311.7.0

WIND BRACING NOTE: PROVIDE DIAGONAL WIND BRACING AT ALL OUTSIDE CORNERS. AT CORNERS WITH LESS THAN 48" OF PANEL WALL, USE ALTERNATE BRACING PANELS IN ACCORDANCE WITH INTERNATIONAL BUILDING CODE FIGURE R602.10.2.2

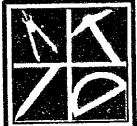

Alternative
Designs Inc.

www.alternativedesigns.net

Residential/Commercial
Design

94 Old Granite Street

Manchester, NH 03101

phone: (603) 645-4388

fax: (603) 645-6010

These drawings, specifications, and the design conveyed are the exclusive property of Alternative Designs Inc. Any form of reproduction of these documents, or of the design, is strictly prohibited. A.D.I. © 2020

Contractor to check & verify all dimensions & structural members before construction. All construction shall be in strict compliance with the State of New Hampshire or Massachusetts Building Code, where applicable.

REVISIONS

26-195
MAY 2026
SHEET 5 OF 9



26-195

A5